
Портфолио Архитектора-дизайнера

Барановой Юлии Геннадиевны

Тел.: +7 925 3048230
tananda2002@inbox.ru

Резюме специалиста:

Баранова Юлия Геннадиевна

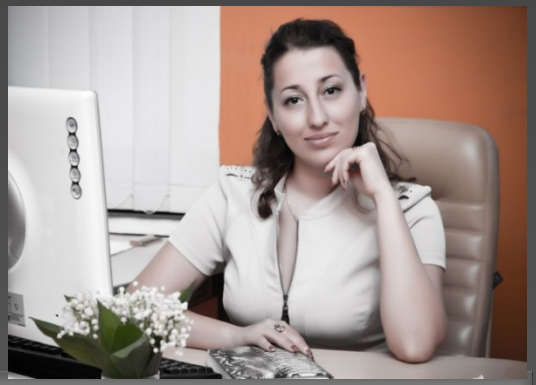

- *1982 года рождения (38 лет)*
- *Не замужем*
- *Готова к командировкам*
- *Есть загран. паспорт, водительское удостоверение.*
- *Тел.: +7 925 3048230*
- *Эл. почта: tananda2002@inbox.ru*
- *Гражданство: РФ*

Цель

Найти интересную работу с возможностью профессионального и карьерного роста. **Образование** - высшее

2000-2006г. Харьковский Государственный Технический Университет Строительства и Архитектуры. Специальность - Архитектор-дизайнер.

Опыт работы (20 лет)

ГК ФСК г. Москва. март. 2023г.-июнь 2026г. Глав.специалист.

ООО «Зак Девелопмент» , г. Москва. окт. 2022г.-март 2023г. Главный специалист-архитектор (рук.группы).

АО «ФЦНИВТ «СНПО «Элерон»(Росатом) , г. Москва. Март. 2019г.-окт. 2022г. Ведущий архитектор.

ООО «Древмаркет Трейд, г. Москва. Янв. 2019г.-фев. 2019г. (2 мес.). Дизайнер.

ООО «Генпроектстрой», г. Москва. Июнь 2014г.-дек. 2018г. (4 года 5 мес.). Ведущий архитектор. ГАП.

ООО «Соло Арт», г. Киев. Янв.2012г.- март 2014г. (2 года 3 мес.). Ведущий архитектор. Дизайнер.

«Югланс», г. Ялта. Янв.2011г.-дек.2011г. (1 год). Архитектор, Дизайнер, авт. надзор, Ведущий менеджер проекта.

ООО ***«НБТ»,*** г. Симферополь. Авг.2010г.-дек.2010г. (5 мес.) Главный инженер.

Freelance. г. Харьков. Июль 2009г.-июль 2010г. (1 год 1 месяц). Архитектор-дизайнер.

ООО фирма ***«Авуар»,*** г. Харьков. Окт. 2005г.-июль 2009г. (3 года 10 мес.). Архитектор-дизайнер.

Языки

Русский – родной, Английский – базовый.

Навыки работы с ПК

ArchiCAD, Revit, AutoCAD, Photoshop, Artlantis, 3D Max, Microsoft Office.

Профессиональные навыки

Проектирование на всех стадиях, визуализация, расчеты (теплотехника, инсоляция), управление рабочими процессами, авторский надзор, презентации, общение с заказчиком, ведение нескольких объектов одновременно, выполнение работ в срок.

Повышение квалификации

Удостоверение о повышении квалификации №00597. Удостоверение № 9-2020/4 по охране труда.

Многоэтажный жилой дом с встроено-пристроенными помещениями торговли и подземной стоянкой.


- ул. Тринклера, г.Харьков





Жилой комплекс с подземной автостоянкой, расположенный по адресу: г. Москва, ул. Мосфильмовская

План подземного этажа на отм. -9.900

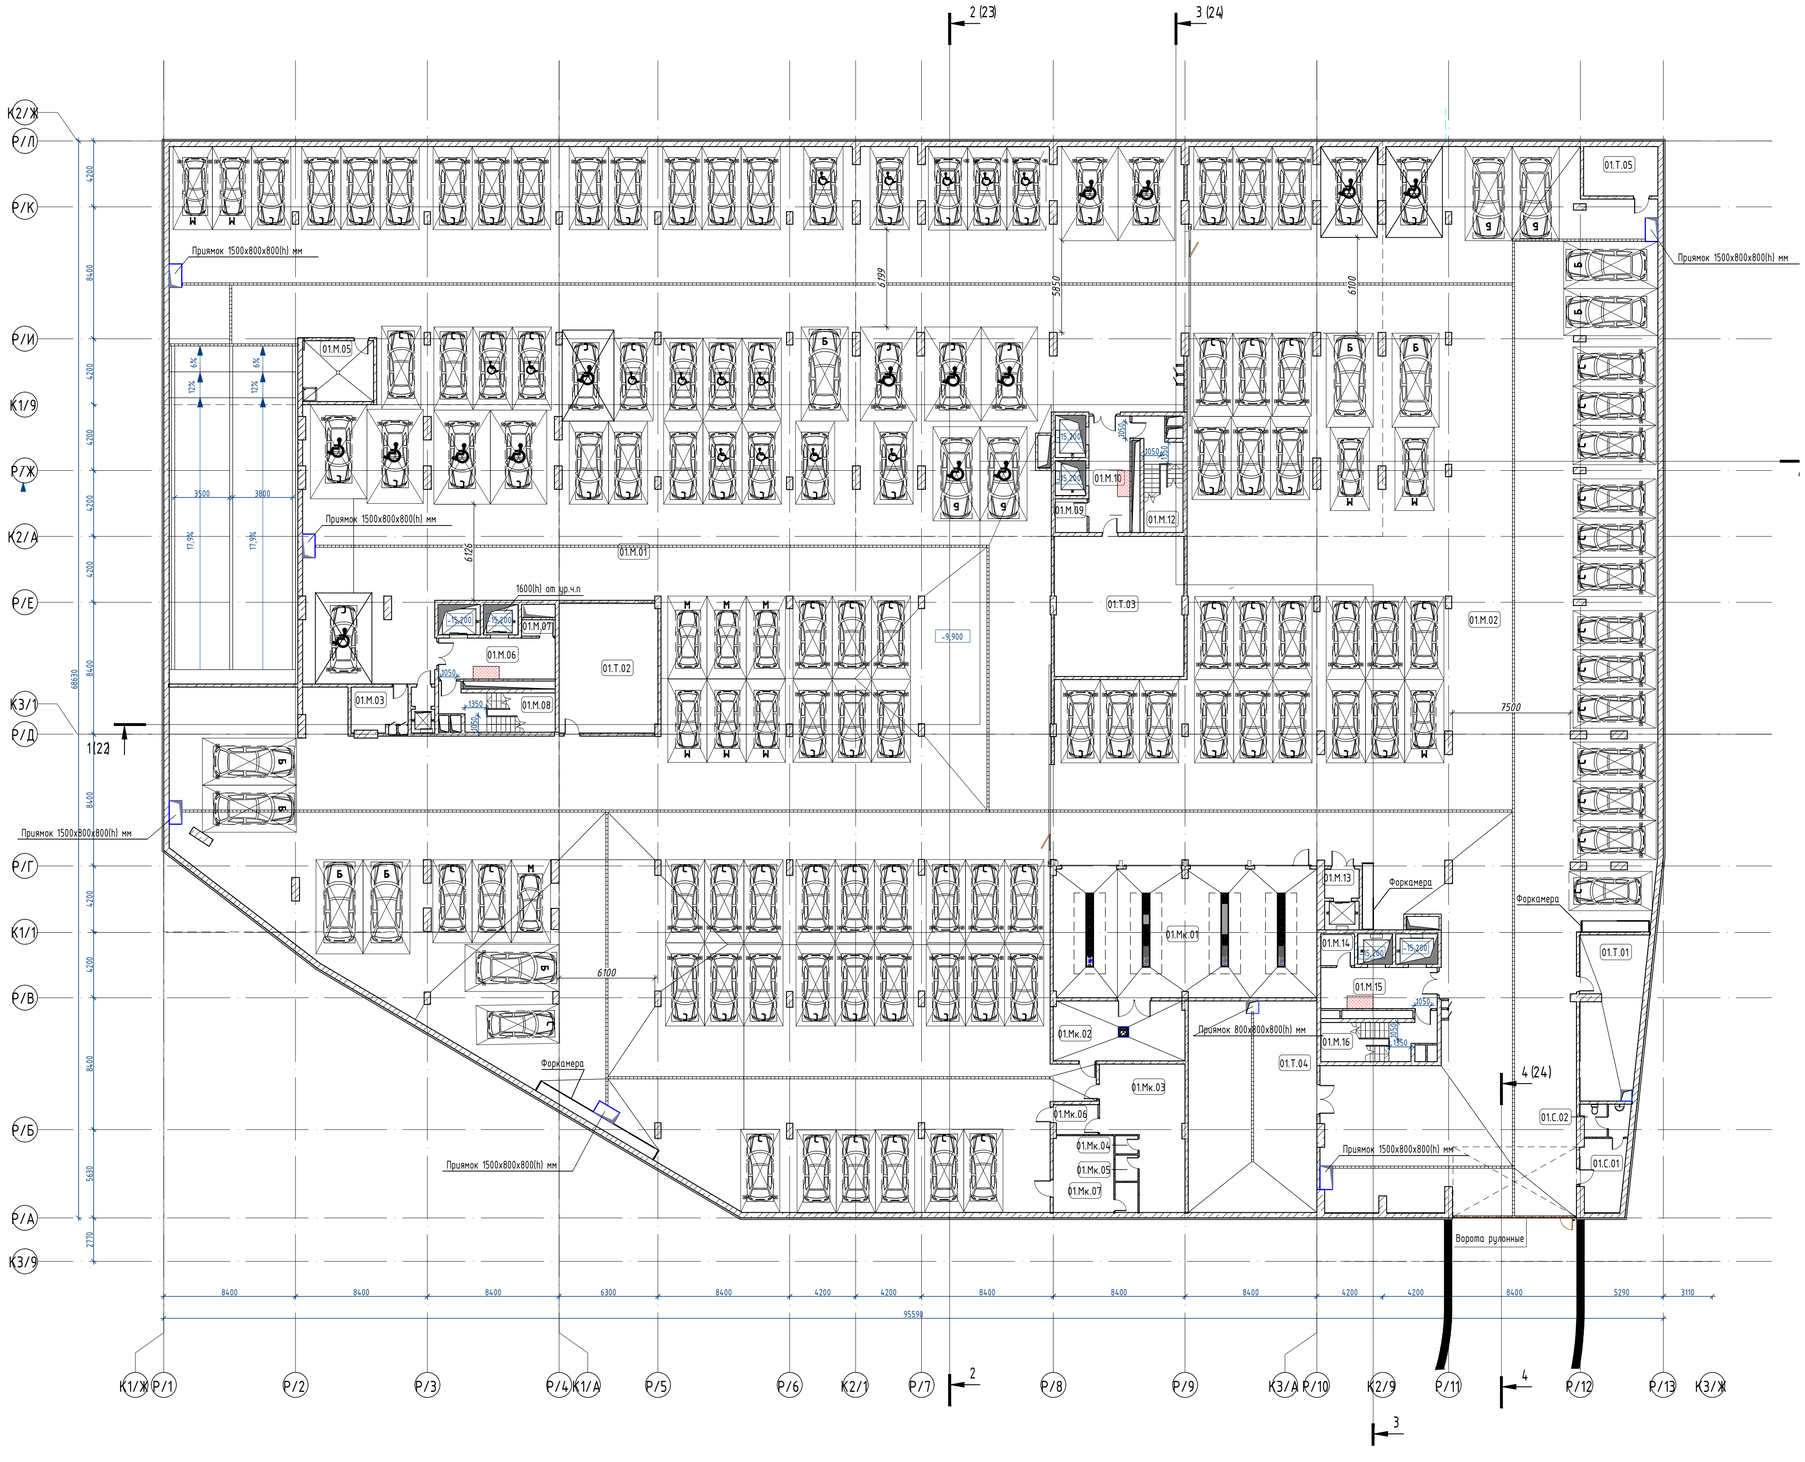

ЭКСПЛИКАЦИЯ ПОМЕЩЕНИЙ -1 ПОДЗЕМНОГО ЭТАЖА		
Номер	Наименование	Площадь
	МОП	
01.М.01	Помещение автостоянки	2203,80
01.М.02	Помещение автостоянки	900,00
01.М.03	Кладовая	9,60
01.М.04	Тамбур-шлюз	1,80
01.М.05	ПУИ	22,80
01.М.06	Тамбур-шлюз	19,40
01.М.07	Кладовая	4,40
01.М.08	Лестничная клетка	15,30
01.М.09	Кладовая	4,40
01.М.10	Тамбур-шлюз	19,40
01.М.11	ПУИ	3,00
01.М.12	Лестничная клетка	15,30
01.М.13	Тамбур-шлюз	4,10
01.М.14	Кладовая	4,40
01.М.15	Тамбур-шлюз	19,40
01.М.16	Лестничная клетка	15,30
01.М.17	ПУИ	3,00
Площадь МОП:		3265,40
	Мойка	
01.Мк.01	Помещение мойки	137,20
01.Мк.02	Техническое помещение мойки	31,90
01.Мк.03	Помещение персонала мойки	46,10
01.Мк.04	С/У персонала	1,70
01.Мк.05	Душевая персонала	2,40
01.Мк.06	Помещение сушильного шкафа	5,60
01.Мк.07	Помещение для клиентов мойки	18,80
Площадь мойки:		246,50
	Служебные помещения	
01.С.01	Помещение охраны	10,20
01.С.02	С/У охраны	8,80
Площадь служебных помещений:		19,00
	Технические помещения	
01.Т.01	Помещение уборочной техники	40,50
01.Т.02	Венткамера	51,80
01.Т.03	Венткамера	73,30
01.Т.04	Мусорокамера	110,50
01.Т.05	ВРУ автостоянки	14,90
Площадь технических помещений:		291,00

Общая площадь машино-мест:	1996,40
Сумма площадей помещений этажа:	5818,30
Общая площадь этажа:	6000,00

Условные обозначения :

+3,200 — Отметка пола

Железобетон


Ячеистый бетон D600 Ytong или аналог 100/200/250/300 мм

Утеплитель Технониколь CARBON PROF или аналог (в зоне промерзания грунта (~2 метра)-100мм, ниже-50мм

Парковочное место для МГН

Зона безопасности для МГН в условиях пожарной опасности

Кладочный план 1 этажа на отм.+0.260

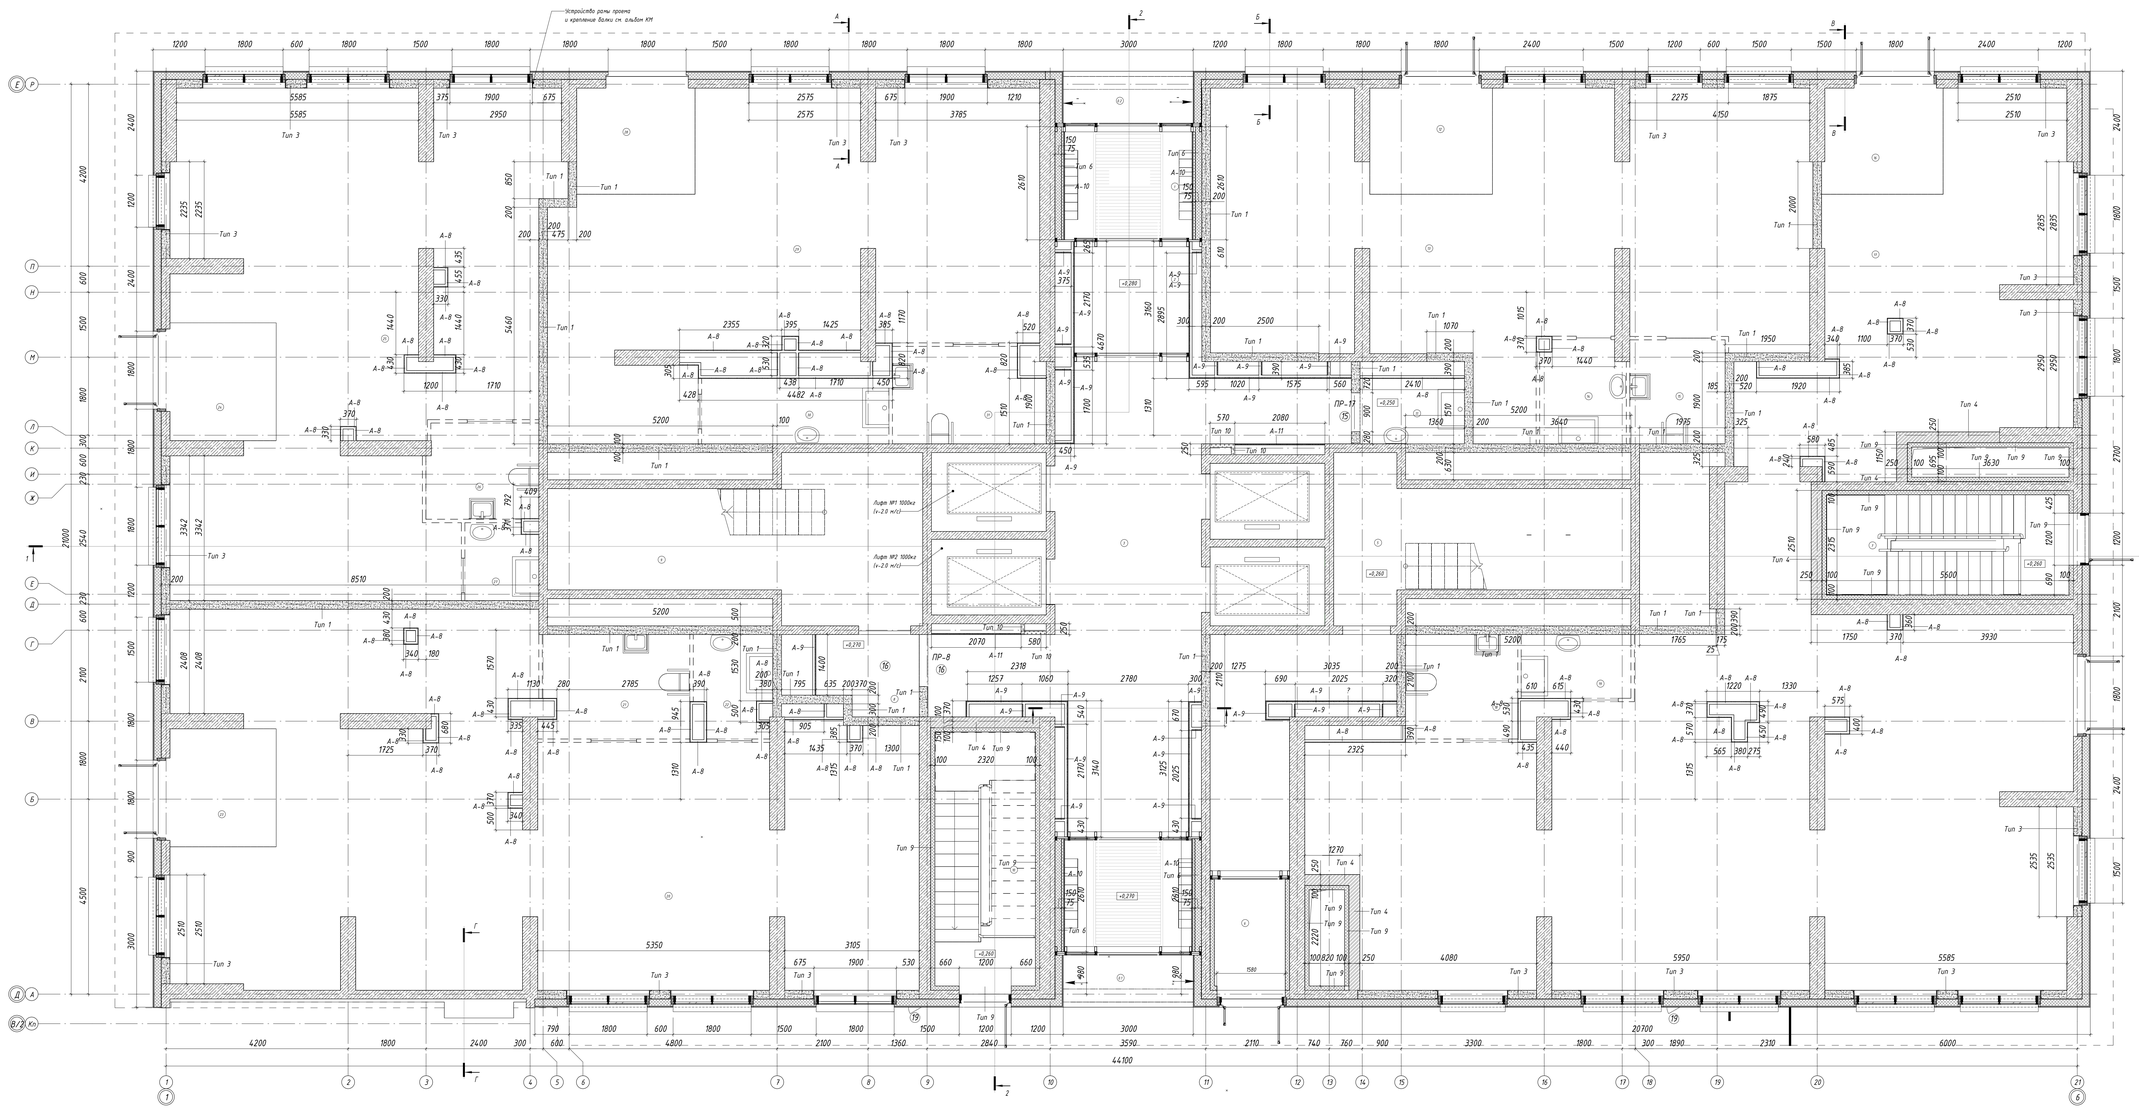

Экспликация помещений

Номер	Наименование	Площадь, м2	Кат. пом.
0.1	Фонарная	2,5	
0.1	Крыльцо	3,7	
0.2	Крыльцо	3,7	
0.2	Фонарная	1,8	
Нежилые помещения для коммерческого использования (Ф4.3) №1			
12	Тамбур	6,9	-
13	Нежилое помещение для коммерческого использования	76,3	-
14	ПУИ	4,6	В4
15	Универсальный санузел	5,3	-
Нежилые помещения для коммерческого использования (Ф4.3) №2			
16	Тамбур	6,7	-
17	Нежилое помещение для коммерческого использования	174,2	-
18	Универсальный санузел	6,2	-
19	ПУИ	3,7	В4
Нежилые помещения для коммерческого использования (Ф4.3) №3			
20	Нежилое помещение для коммерческого использования	113,9	-
21	Универсальный санузел	8,1	-
22	ПУИ	4,0	В4
23	Тамбур	6,7	-
Нежилые помещения для коммерческого использования (Ф4.3) №4			
24	Тамбур	6,7	-
25	Нежилое помещение для коммерческого использования	82,1	-
26	Универсальный санузел	5,7	-
27	ПУИ	3,0	В4
Нежилые помещения для коммерческого использования (Ф4.3) №5			
28	Тамбур	6,7	-
29	Нежилое помещение для коммерческого использования	64,8	-
30	ПУИ	6,5	В4
31	Универсальный санузел	7,5	-
Помещения общего доступа			

Экспликация помещений

Номер	Наименование	Площадь, м2	Кат. пом.
1	Лифтовой холл (тамбур-шлюз)	40,5	-
1	Тамбур	7,8	-
2	Тамбур	7,0	-
2	Лестничная клетка	12,7	-
2	Коридор	81,9	-
3	Коридор	65,7	-
3	Лобби	44,8	-
3	Лестничная клетка	13,4	-
4	Тамбур-шлюз	10,0	-
4	Тамбур	8,2	-
5	Лестничная клетка	12,7	-
5	Лестничная клетка	32,5	-
6	Лестничная клетка	13,4	-
6	Тамбур	4,2	-
7	Лестничная клетка	13,1	-
8	Тамбур-шлюз	4,1	-
9	Лестничная клетка	25,7	-
10	Лестничная клетка	13,4	-
Технические помещения			
1	Техническое пространство для прокладки инженерных коммуникаций	784,5	-
7	Помещение СС	19,0	В3
8	Помещение для прокладки инженерных коммуникаций	6,2	В4
9	Венткамера	39,6	Д
10	Техническое помещение	18,5	В4
11	Объектовый пункт пожаротушения	5,2	В4
11	ПУИ	3,6	В4
12	Техническое помещение	5,9	В4
13	Венткамера	41,1	Д
14	Электрощитовая жилой части	19,1	В3
15	Электрощитовая нежилой части	13,6	В3
16	Электрощитовая автостоянки	23,8	В3
17	Помещение уборочной техники	10,2	В4
Итого:		2012,8	

Спецификация дверных проемов в архитектурных стенах и перегородках 1 этажа

Поз.	Габариты, мм: Ширина	Габариты, мм: Высота	Кол.	Отм. низа	Примечание
15	900	2085	1	+0,170	
16	1200	2085	1	+0,160	
19	300	300	2	+0,848	

Спецификация дверных проемов в железобетонных стенах 1 этажа

Поз.	Габарит проема, мм: Ширина	Габарит проема, мм: Высота	Отм. низа проема от плиты	Кол-во шт	Примечание
16	1200	2085	+0,270	1	

Ведомость перемычек дверных проемов

Марка	Эскиз	Длина, мм	Кол-во, шт.
ПР-8	250; Блок силикатный полнотелый; Отм. низа; L50x6	1750	1
ПР-17	250; Блок силикатный полнотелый; Отм. верх. пр.; L50x6	1450	1

Спецификация расхода материалов

Поз.	Обозначение	Наименование	Кол. м2	Масса ед., кг	Объем м3
Тип 1	ГОСТ 31360-2007	Блоки газобетонные стеновые 600x200x250(h) D600 на клею	311,0		62,20
Тип 3	ГОСТ 31360-2007	Блоки газобетонные стеновые D600 на клею 200мм с штукатуркой 20 мм с одной стороны	124,6		24,92
Тип 4	ГОСТ 379-2015	Силикатный полнотелый блок (СБПо-М150/1,8 498x250x248 ГОСТ 379-2015, марка по прочности М150, класса средней плотности 1,8)	50,8		12,69
Тип 6	ГОСТ 32314-2012	Минераловатный утеплитель (ρ=110-130 кг/м^3, предел прочности на отрыв не менее 15 кПа, λ=0,04 Вт/(м*С) - 150 мм	45,3		6,80
Тип 9	ГОСТ 32314-2012	Минераловатный утеплитель (ρ=110-130 кг/м^3, предел прочности на отрыв не менее 15 кПа, λ=0,04 Вт/(м*С) - 100 мм	203,5		20,35
Тип 10	ГОСТ 6428-2018, ТУ 5742-003-78667917-2005	Гипсовые пазогребневые плиты влагостойкие полнотелые	6,7		0,54

Спецификация элементов на 1 перемычку 1 этажа

Поз.	Обозначение	Наименование	Длина, мм	Кол.	Масса ед. кг,кг	Примечание
ПР-8						
	ГОСТ 8509-93	L 40x4	1750	2	4,24	
	ГОСТ 8509-93	L 70x6	200	2	1,28	
	Каталог МКТ	Анкер-болт		4		
ПР-17						
	ГОСТ 8509-93	L 40x4	1450	2	3,51	
	ГОСТ 8509-93	L 70x6	200	2	1,28	
	ГОСТ 103-2006	Стальная полоса 40x4	180	6	0,23	

Спецификация перегородок из гипсовых плит на металлическом каркасе


Марка	Наименование	Площадь, м2	Объем, м3	ГОСТ, ТУ
А-8	Зашивка (тип С 625) на металлическом каркасе (профиль ПН 50x40 и ПС 50x50), с облицовкой листом ГСП-А - 12,5 мм (с одной стороны), без ваты	227,7	14,23	ГОСТ 32614-2012
А-9	Зашивка (тип С 626) на металлическом каркасе (профиль ПН 50x40 и ПС 50x50), с облицовкой 2 листами ГСП-А - 12,5 мм (с одной стороны), без ваты	128,1	9,61	ГОСТ 32614-2012
А-10	Зашивка (тип С 626) на металлическом каркасе (профиль ПН 50x40 и ПС 50x50), с заполнением минераловатной плитой ρ=38 кг/м.куб. - 50 мм, с облицовкой 2 листами ГСП-А - 12,5 мм (с одной стороны)	42,8	3,21	ГОСТ 32314-2012, ГОСТ 32614-2012
А-11	Зашивка на металлическом каркасе с облицовкой 2 листами ГВЛ 12,5 мм (с одной стороны)	18,0	0,45	ГОСТ 32614-2012

УСЛОВНЫЕ ОБОЗНАЧЕНИЯ:

- монолитные ж.б. конструкции
- блоки газобетонные стеновые D600 на клее 600x200x300(h) /600x100x300(h) мм
- минераловатный утеплитель
- утеплитель из экструдированного пенополистирола по наружному контуру стен
- блок силикатный полнотелый - 250 мм
- перегородка с сборным проемом, монтируемая собственником помещения

ПРИМЕЧАНИЯ:

1. Данный лист см. совместно с л. 1-2 (Общие данные);
2. Отметка уровня верха плиты перекрытия над техническим пространством корпуса 13.1 принята +0,160, рабная абсолютно отметке 128,25;
3. Перед началом кладочных работ устроить фахверки в наружных стенах по типу 3 согласно комплекту КМ;
4. Все отметки на плане указаны с учетом конструкции чистого пола;
5. Отметка прямоугольных отверстий дана от верха плиты перекрытия этажа до низа отверстий; отметка круглых отверстий, гильз дана от верха плиты перекрытия этажа до центральной оси отверстий;
6. Данный лист см. совместно с комплектом КЖ, привязку отверстий в ж.б. конструкциях см. комплект КЖ;
7. Сводную спецификацию материалов стен и перегородок и сводную ведомость перемычек см. комплект АР1.4.ПЗ;
8. Зашивка проектных коммуникаций 1 этажа в ПОН выполнить из перегородок типа С625, профиль ПН 50x40 и ПС 50x50, один лист ГСП-А 12,5 мм с одной стороны, без ваты, общей толщиной 62,5 мм (тип А-8);
9. Зашивки в лобби выполнить из перегородок типа С626, ГСП-А 12,5 мм 2 слоя + профиль ПН 50x40 и ПС 50x50, без ваты, общей толщиной 75 мм (тип А-9);
10. Данный комплект выпущен без учета инженерных отверстий в стенах и перекрытии разделов ОВ, ВК, ЭОМ, СС.

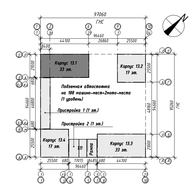

0,000 = 128,09

						ZD-МОС-ИЛО-Р-22 -АР1.1			
						Многоэтажные жилые дома корпус 13.1 – 13.4 с подземной автостоянкой в составе комплексной общественно-жилой застройки по адресу: г. Москва, ул. Ивовайская, вл.2Б			
Изм.	Кол.уч.	Лист	№ док.	Подпись	Дата				
Разработал		Баранова			01.12.22	Корпус 13.1	Стадия	Лист	Листов
Проверил		Грачев			01.12.22		Р	5	
Н. контр.		Муравьева			01.12.22				
ГАП		Грачев			01.12.22	Кладочный план 1 этажа на отм.+ 0.260	ООО "Зак Девелопмент"		
ГИП		Липовских			01.12.22				

Согласовано

Инв. № подл. | Подп. и дата | Взам. инв. №

Копирование без разрешения ООО "Зак Девелопмент" запрещено

Формат А3


Разрез 2-2

Грунтовка глубокого проникновения	
Шлифовка неровностей	
Плита ж.б. (см. раздел КЖ)	– 200 мм

Керамогранит с затиркой швов	– 8мм
Водостойкий плиточный клей	– 6мм
Цементно-песчаная стяжка М150, армированная	
сеткой 5Вр1 с ячейкой 100х100мм	– 86мм
Ж.б. плита (см. раздел КЖ)	– 200мм

Финишное покрытие пола (выполняется собственником помещения)	– 20мм
Цементно-песчаная стяжка М150,	
армированная сеткой 5Вр1 с ячейкой 100х100	– 60мм
Полиэтиленовая пленка 200 мкр	
Минераловатный утеплитель (ρ=99-121 кг/м^3, предел прочности	
на сжатие не менее 25 кПа, λ=0,041 Вт/м°С)	– 40мм
Ж.б. плита (см. раздел КЖ)	– 200 мм

Керамическая фасадная плитка 288х88мм	– 8 мм
Плиточный клей (шов 12 мм)	– 15 мм
Штукатурно-клеевой слой	– 5 мм
Тарельчатые дюбели со стальным сердечником	
Фасадная стеклотканевая щелочная сетка М3600	– 1 слой
Базовый штукатурный слой	– 5 мм
Минераловатный утеплитель, ρ=110-130 кг/м^3, λ=0,041 Вт/м°С	– 160 мм
Клей для крепления утеплителя	– 5 мм
Выравнивающая цементная штукатурка	– 0-30 мм
Ж.б. стена (см. раздел КЖ) / Газобетонные блоки D600	– 200 мм

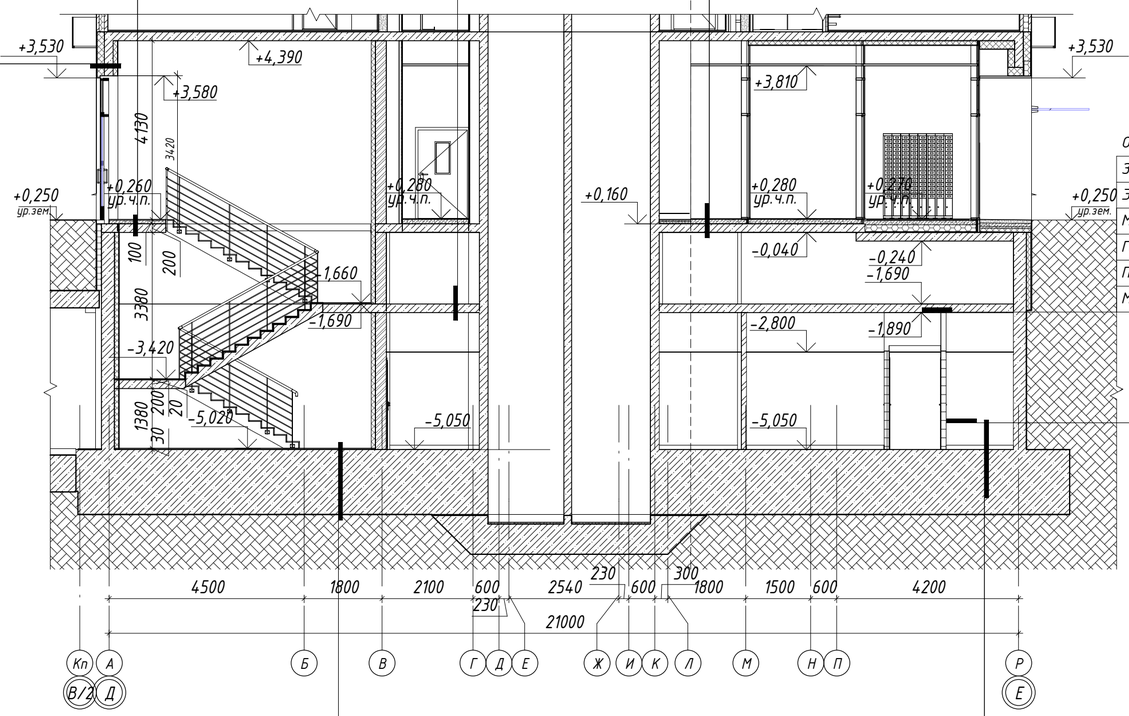


Обратная засыпка (непучинистый грунт)	
Защитная мембрана "Planter Standart" или аналог	– 8 мм
Экструдированный пенополистирол, л=0,032 Вт/мК	– 100 мм
Мастика приклеивающая	
Гидроизоляция "Технопласт ЭПП" или аналог	– 2 слоя
Праймер битумный	
Монолитная ж.б. стена (см. раздел КЖ)	– 300 мм

Обратная засыпка (непучинистый грунт)	
Защитная мембрана "Planter Standart" или аналог	– 8 мм
Гидроизоляция "Техноэласт ЭПП" или аналог	– 2 слоя
Праймер битумный	
Монолитная ж.б. стена (см. раздел КЖ)	– 300 мм

Керамогранит с затиркой швов	– 8 мм
Водостойкий плиточный клей	– 22 мм
Шлифовка неровностей	
Фундаментная плита (см. раздел КЖ)	– 1500 мм

Грунтовка глубокого проникновения	
Шлифовка неровностей	
Фундаментная плита (см. раздел КЖ)	– 1500 мм

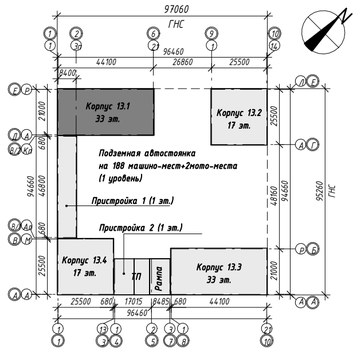

Условные обозначения:

- – монолитные ж/б конструкции
- – минераловатный утеплитель
- – Плита силикатная пазогребневая пустотелая – 115 мм
- – Блок силикатный полнотелый – 250 мм
- – блок силикатный полнотелый – 250 мм
- – Грунт

Примечания:

1. Данный лист см. совместно с разделом КЖ;
2. Устройство гидроизоляции наружных стен подземного этажа и расход материалов см. раздел КЖ;
3. Металлические ограждения лестниц см. альбом КМ;
4. Потолок в подвале выполнен из металической сетки (см. ведомость отделки)

Согласовано

Взам. инв. №

Подп. и дата

Инв. № подл.

Изм.	Кол.уч.	Лист	№ док.	Подпись	Дата	ZD-МОС-ИЛО-Р-22 -АР1.1			
						Многоэтажные жилые дома корпус 13.1 - 13.4 с подземной автостоянкой в составе комплексной общественно-жилой застройки по адресу: г. Москва, ул. Иловайская, вл.2Б			
Разработал		Баранова			01.12.22	Корпус 13.1	Стадия	Лист	Листов
Проверил		Грачев			01.12.22		Р	10	
Н. контр.		Муравьева			01.12.22				
ГАП		Грачев			01.12.22	Разез 2-2	ООО "Зак Девелопмент"		
ГИП		Липовских			01.12.22				

Время печати: 01.12.2022 18:36:16

Реконструкция нежилых помещений с надстройкой и пристройкой. Офисный центр

- ул. Ахсарова4/6А, г.Харьков



Разработка ЭП, РП, авторский надзор, разработка интерьеров и мебели.










Жилой комплекс с объектами инфраструктуры

ул. Деревянко, ул. Сумгаитская, г.Харьков

Концепция с анализом территории.

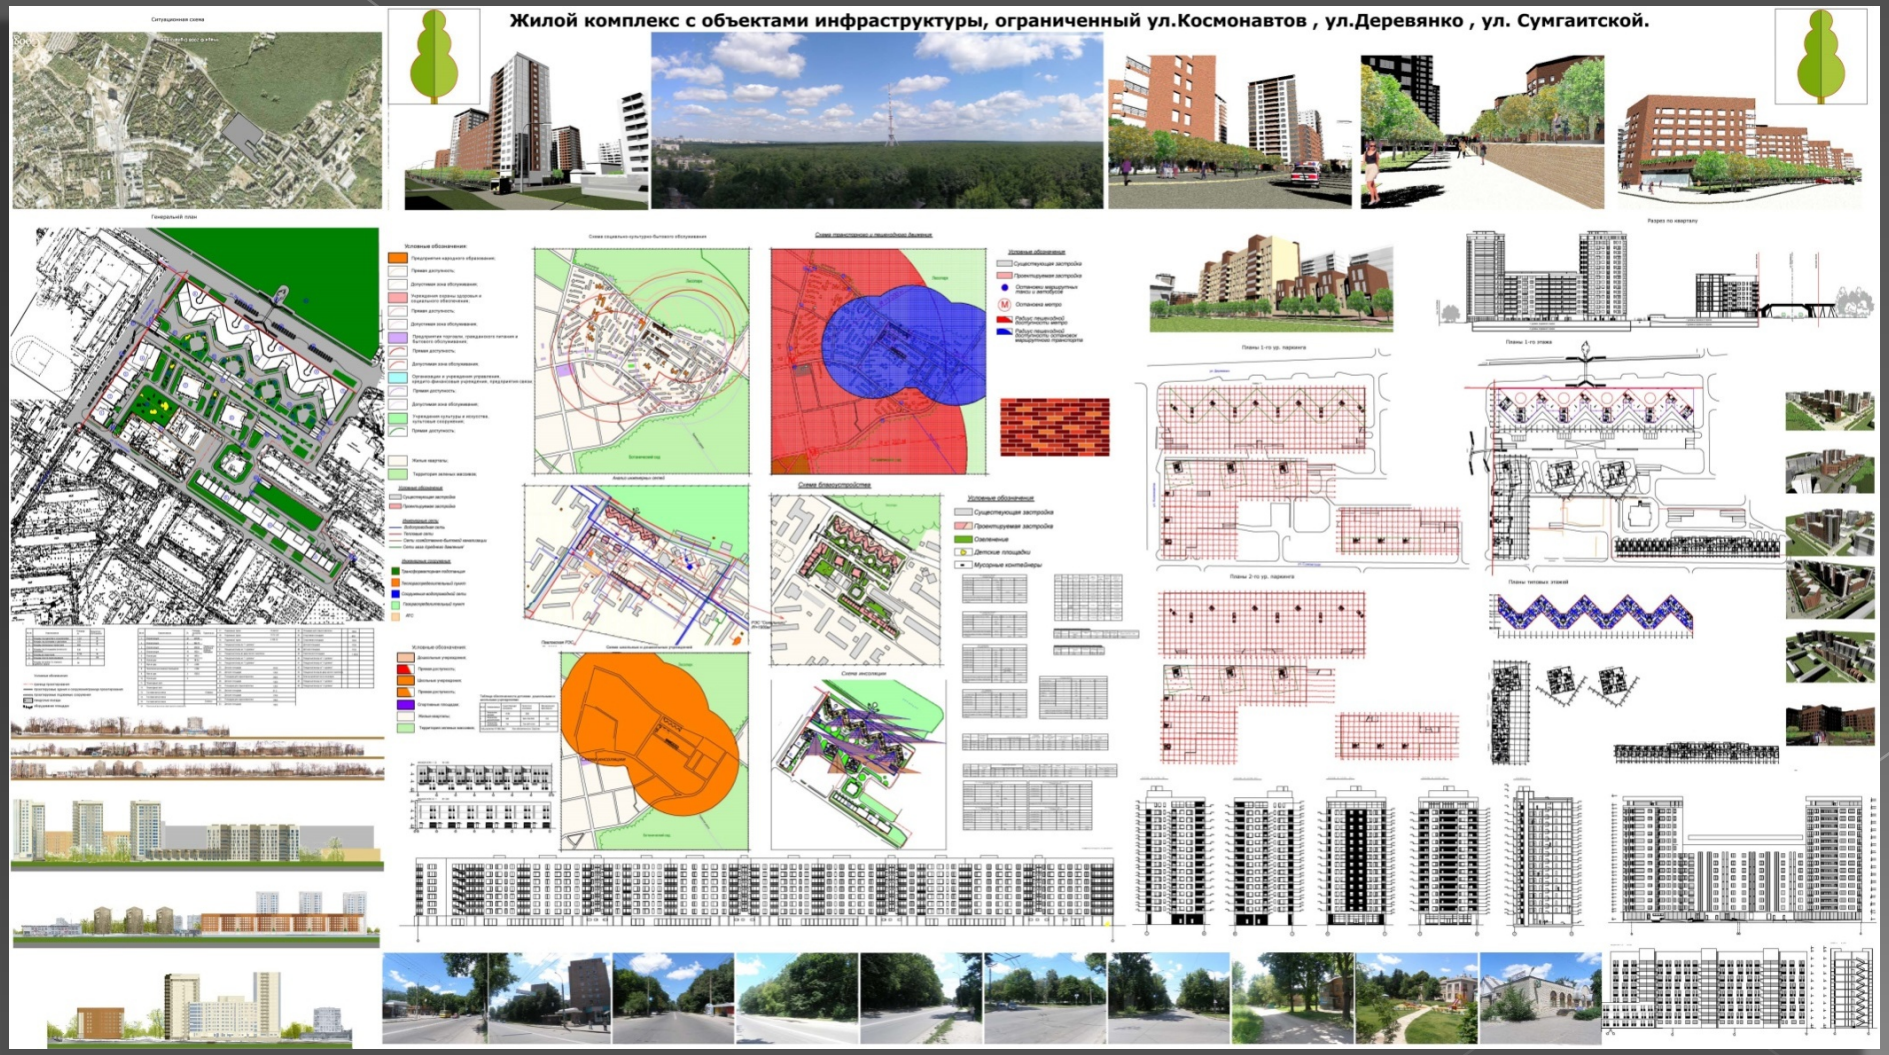

Торгово-развлекательний центр • ул. Квитки Основьяненко, г. Харьков

Эскизный проект.







Торгово-офисный центр • ул. Артема, г. Харьков

Реализация



Визуализация





Стадия П, Р. Авторский надзор



Жилой дом (реконструкция)

ул. Лермонтова, г. Ирпень

Стадия ЭП, Р. Авт. надзор.







Жилой дом (1 очередь)

- **ул. Лесная, г. Ирпень**

Стадия ЭП.

Проект житлового будинку
по вул. Лісова 42, 44
в м. Ірпінь Київської обл.

Период строительства 2013 - 2014г









Развлекательный комплекс «Компас» ◉ ул. Академіка Павлова, 150, г. Харьков

Фасады. ЭП. РП.

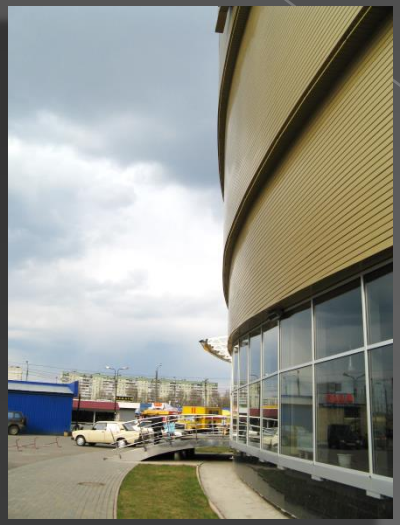

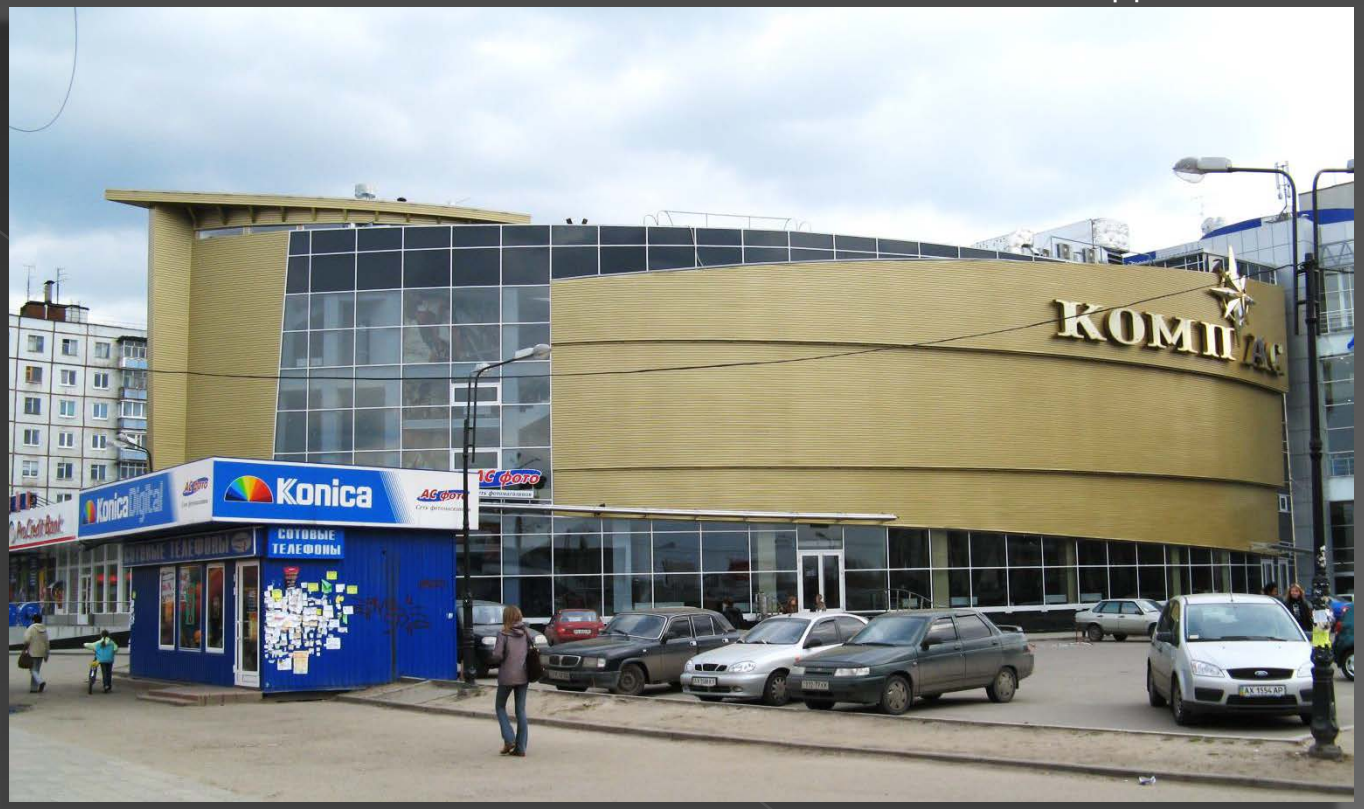







Интерьер ресторана «Компас»

ул. Академика Павлова, 150, г. Харьков

Дизайн проект. Авторский надзор.













Жилой дом

- **вул. Радянська, м. Ірпінь Київської області**

Реализация.



Визуализация.



Разработка всех стадий проекта.

Авторский надзор





Жилой дом

- ул. Матросова, г. Ирпень, Киевская область.

Стадия П, Р.







Жилой дом

- ул. Шевченка, г. Вышгород. Киевская область.

Концепция









Жилой дом

г. Буча. Киевская область.











Стадия П, Р. Авторский надзор

Жилой дом

ул. Карла Маркса, г. Ирпень. Киевская область.

Стадия П, Р.



Общежитие

- Россия

Стадия ЭП, П, Р.



Многофункциональный комплекс

Россия

Концепт. Стадия, П, Р.





Торговый центр

М. Холодная гора г. Харьков.




Концепция



Торговый центр ◉ г. Киев.

Стадия, П, Р.



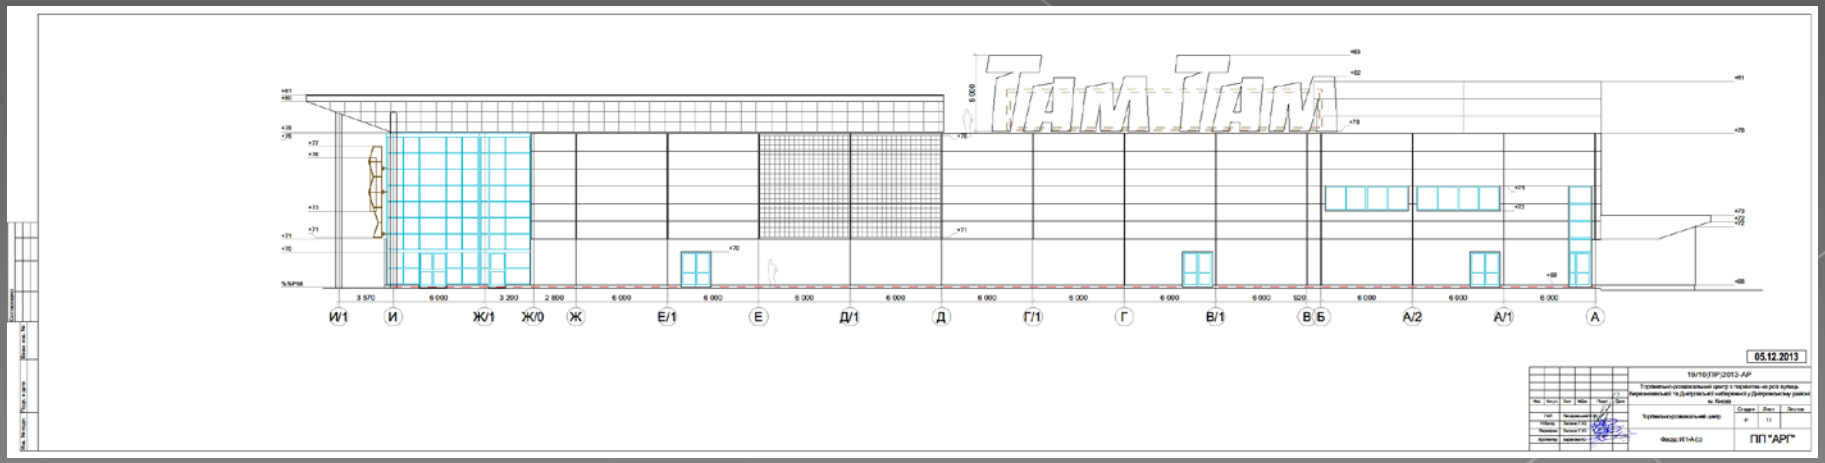

Жилой дом ◉ г. Харьков.



Стадия П, Р.
Авторский надзор



Жилой дом

Реализация

- ул. Львовская, г. Ирпень

Стадия Р. Авторский надзор












Жилой дом (реконструкция)

г. Харьков.

Стадия П.

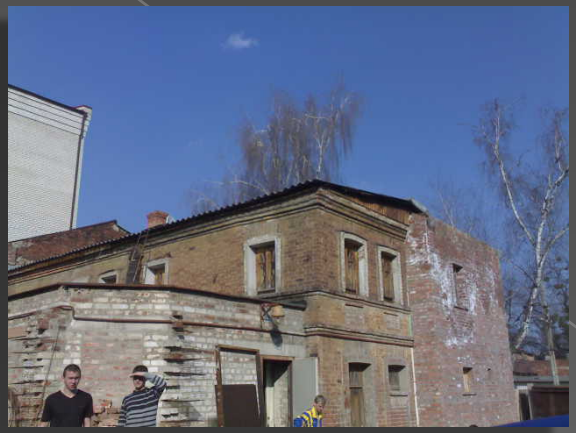









Интерьер квартиры

г. Ирпень, Киевская область.

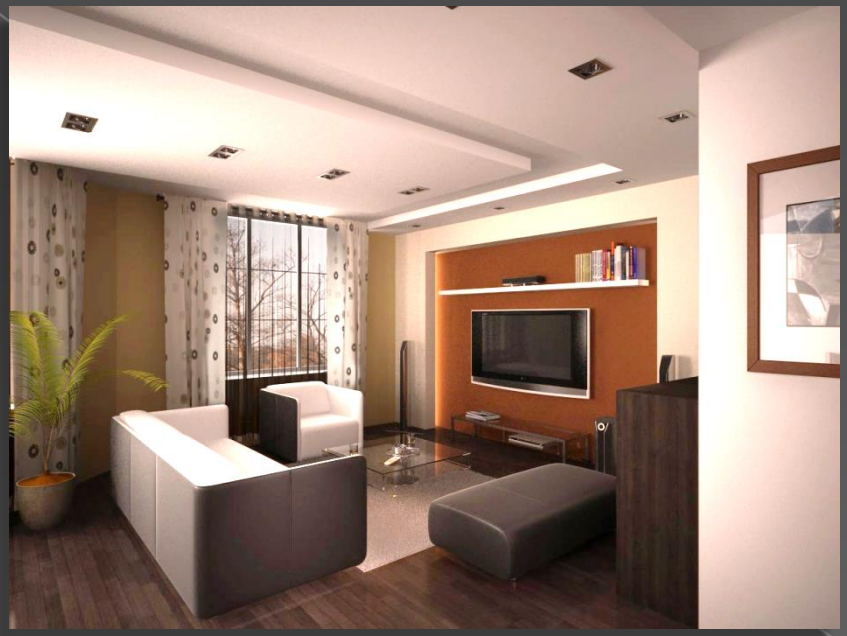





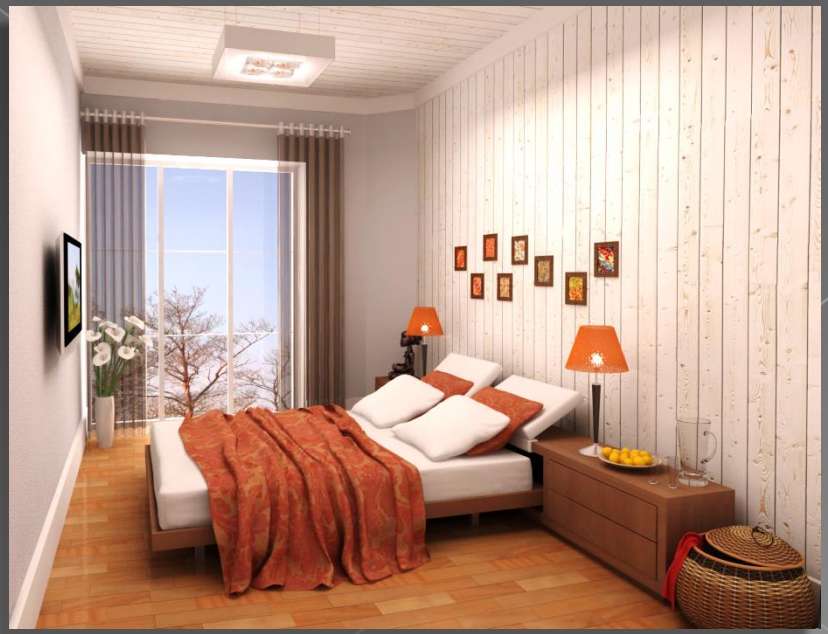


Интерьер квартиры

г. Ирпень, Киевская область.







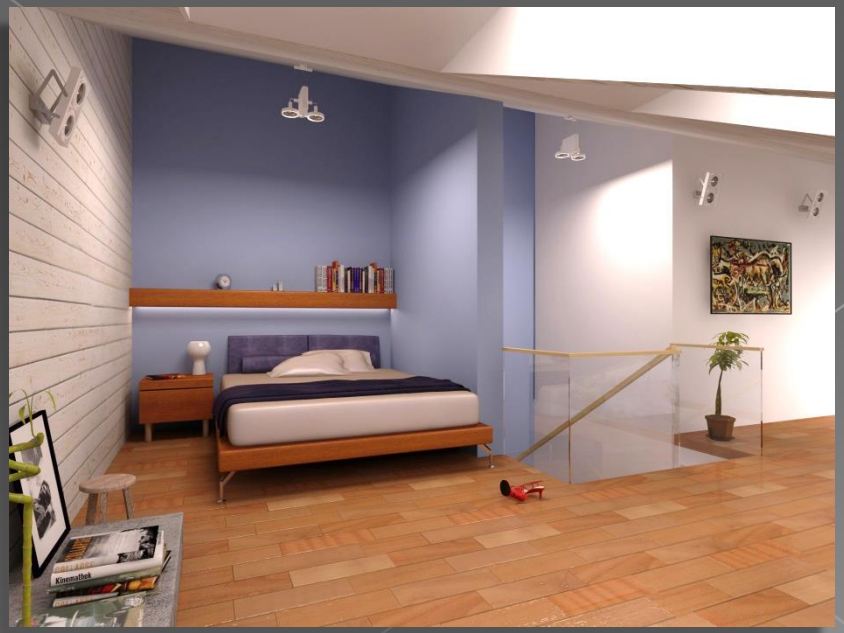

Интерьер комнаты

г. Харьков.





Интерьер комнаты

г. Харьков.



Интерьер комнаты

г. Харьков.





Интерьер холла и переговорной

- г. Москва.









Сквер «Мира»

г. Ирпень. Киевская область.

СКВЕР "МИРУ"







ІСНУЮЧА СИТУАЦІЯ по вул. МИРУ





СИТУАЦІЙНА СХЕМА



СИТУАЦІЙНИЙ ПЛАН



ПЕРЕХРЕСТЯ вул. МИРУ і вул.8 БЕРЕЗНЯ





Умовні позначення:

- Житлові будинки
- Нежитлові споруди
- Дит. садок
- Місце розташування об'єкту





ГЕНЕРАЛЬНИЙ ПЛАН М1:200



СХЕМА РОЗПЛАНУВАННЯ



Умовні позначення:

- Дороги, проїзди з асфальтобетонним покриттям
- Вимощення (тротуари)
- Газон, озеленення
- Відсипка крихтою мелкового щебеню фр.10-20 мм
- Відсипка чорною мармуровою крихтою фр.10-20 мм
- Газонна решітка з газоном
- Плитка тротуарна
- Бруківка "1"
- Бруківка "2"
- Покриття дитячого майданчика
- Хвойні існуючі дерева
- Листяні існуючі дерева

Експлікація:

1. Вхідна група - арка
2. Бювет
3. Існуюча будівля сверловини
4. Дитячий майданчик
5. Альтанка
6. Тимчасова парковка
7. Велопарковка
8. Спорт. майданчик













ІСНУЮЧА СИТУАЦІЯ ПО вул. 8-го БЕРЕЗНЯ



Благоустройство частного дворика

г. Ялта, АР Крым



